0949 Проект

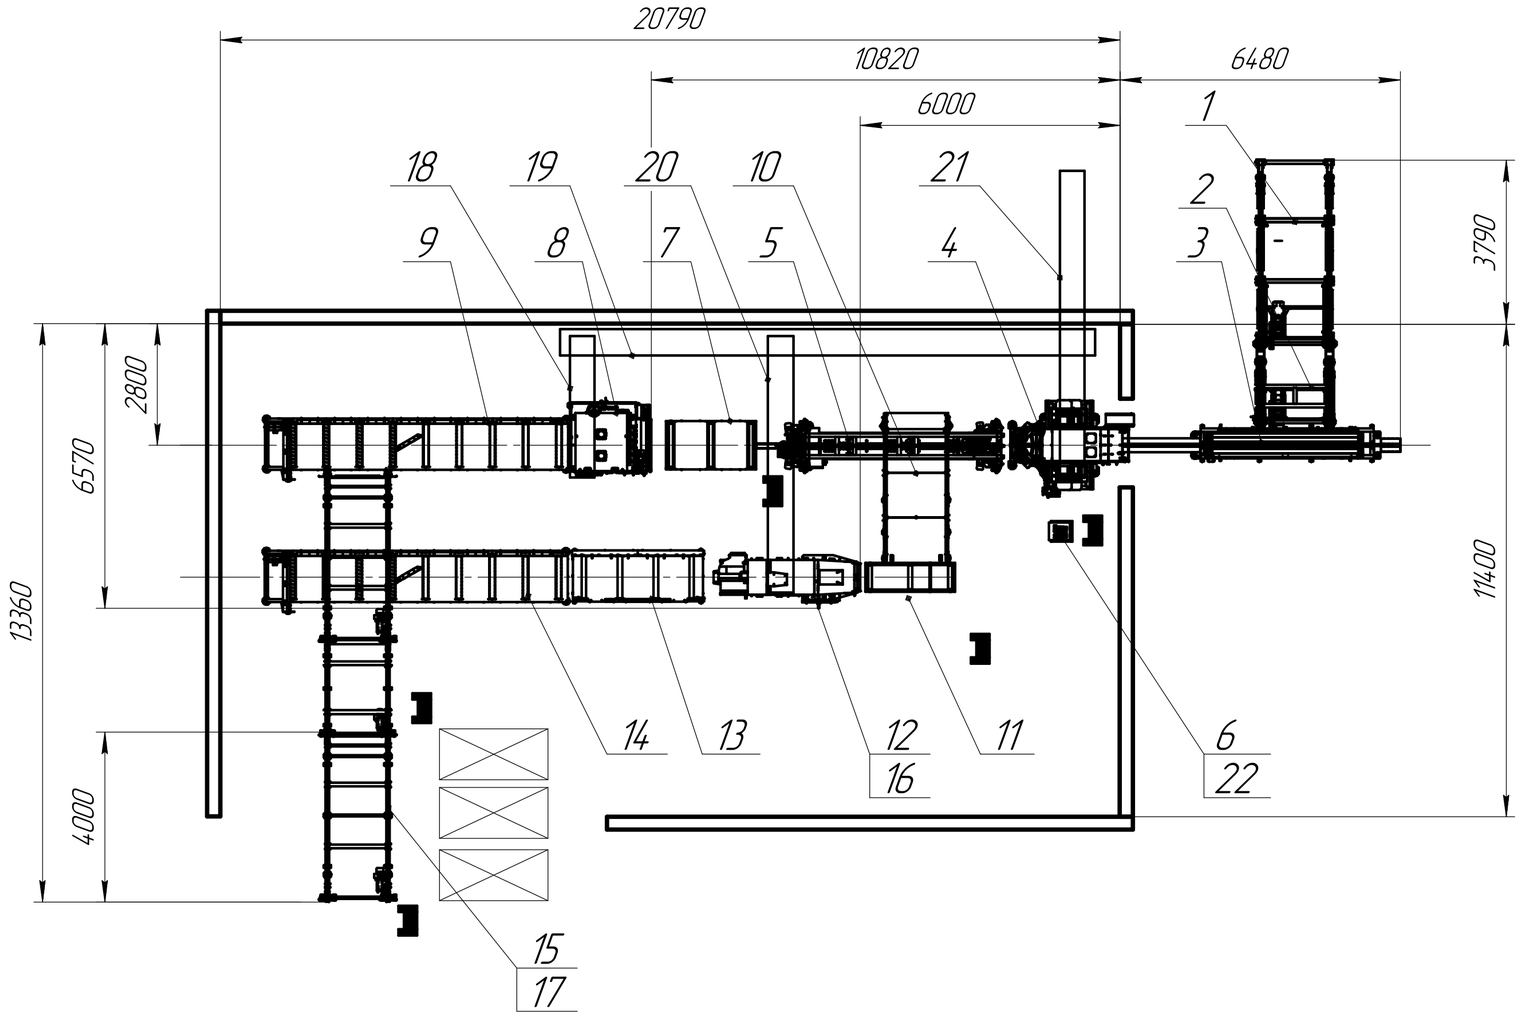

Поз.	Наименование	Кол-во	Примечание
1	Накопитель для бревен НБ25Т 3-4***	1	
2	Перегружатель бревен ПБ-3	1	
3	Стол-комплект С47 ЗУБ_Вр-7 СБ	1	
4	Промышленный бревнопильный станок Триумф Т450_22-30 без стола	1	
5	Отделитель горбыля ОГ-250-3 У без ЭРД***	1	
6	С47 Комплексное управление оборудованием	1	Упр: 1-5
7	Рольганг закрытый Р-1000-2 Усиленный***	1	
8	Кромкообрезной многопильный станок Триумф М1000 Line_37	1	
9	Рольганг винтовой РВ 1000-3Л***	1	Упр: ПМ
10	Транспортер угловой ТУР 2х3	1	
11	Рольганг закрытый Р-550-2	1	
12	Горбыльно-перерабатывающий станок Триумф ГС 4 15 кВт	1	
13	Рольганг приводной РП-1000-3 Вставка	1	
14	Рольганг винтовой РВ 1000-3Л***	1	
15	Транспортерный комплекс поперечный ТКП2-424	1	
16	Пульт управления ТР-2.24-02	1	Упр: 10,14
17	Пульт управления ТР-3.34-01_ПЧ	1	Упр: 15
18	Конвейер скребковый КС 400 (3х1м)	1	
19	Конвейер скребковый КС 400 (2х2,5м+1х1м)	1	
20	Конвейер скребковый КС 340 (4х2,5+1х1м)	1	
21	Конвейер скребковый КСП 500 (2х2,5м+3х1м)	1	
22	Пульт управления ТР-4-46-01	1	Упр: 18-21

Полный комплект технической документации предоставляется после согласования предварительной схемы.
Для установки трансопртеров необходимы траншеи.

Параметры вход. материала:
Высота вход. окна = max 450 мм,
L = от 2м до 3м.
Потребление линии до 230 кВт. (зависит от комплектации)
Производительность до 8 куб.м./час. (зависит от комплектации).

					0949 Проект			
Изм.	Лист	№ докум.	Подп.	Дата	Для ознакомления	Лит.	Масса	Масштаб 1:100
Разраб.		Шишкин Е.А.						
Пров.						Лист	Листов 1	
Т.контр.								
Н.контр.					Приложение 1	ООО "Завод"Энерготех"		
Утв.								

Перв. примен. | Справ. № | Подп. и дата | Инв. № дубл. | Взам. инв. № | Подп. и дата | Инв. № подл.

Копировал | Формат А2