0948-2 Проект

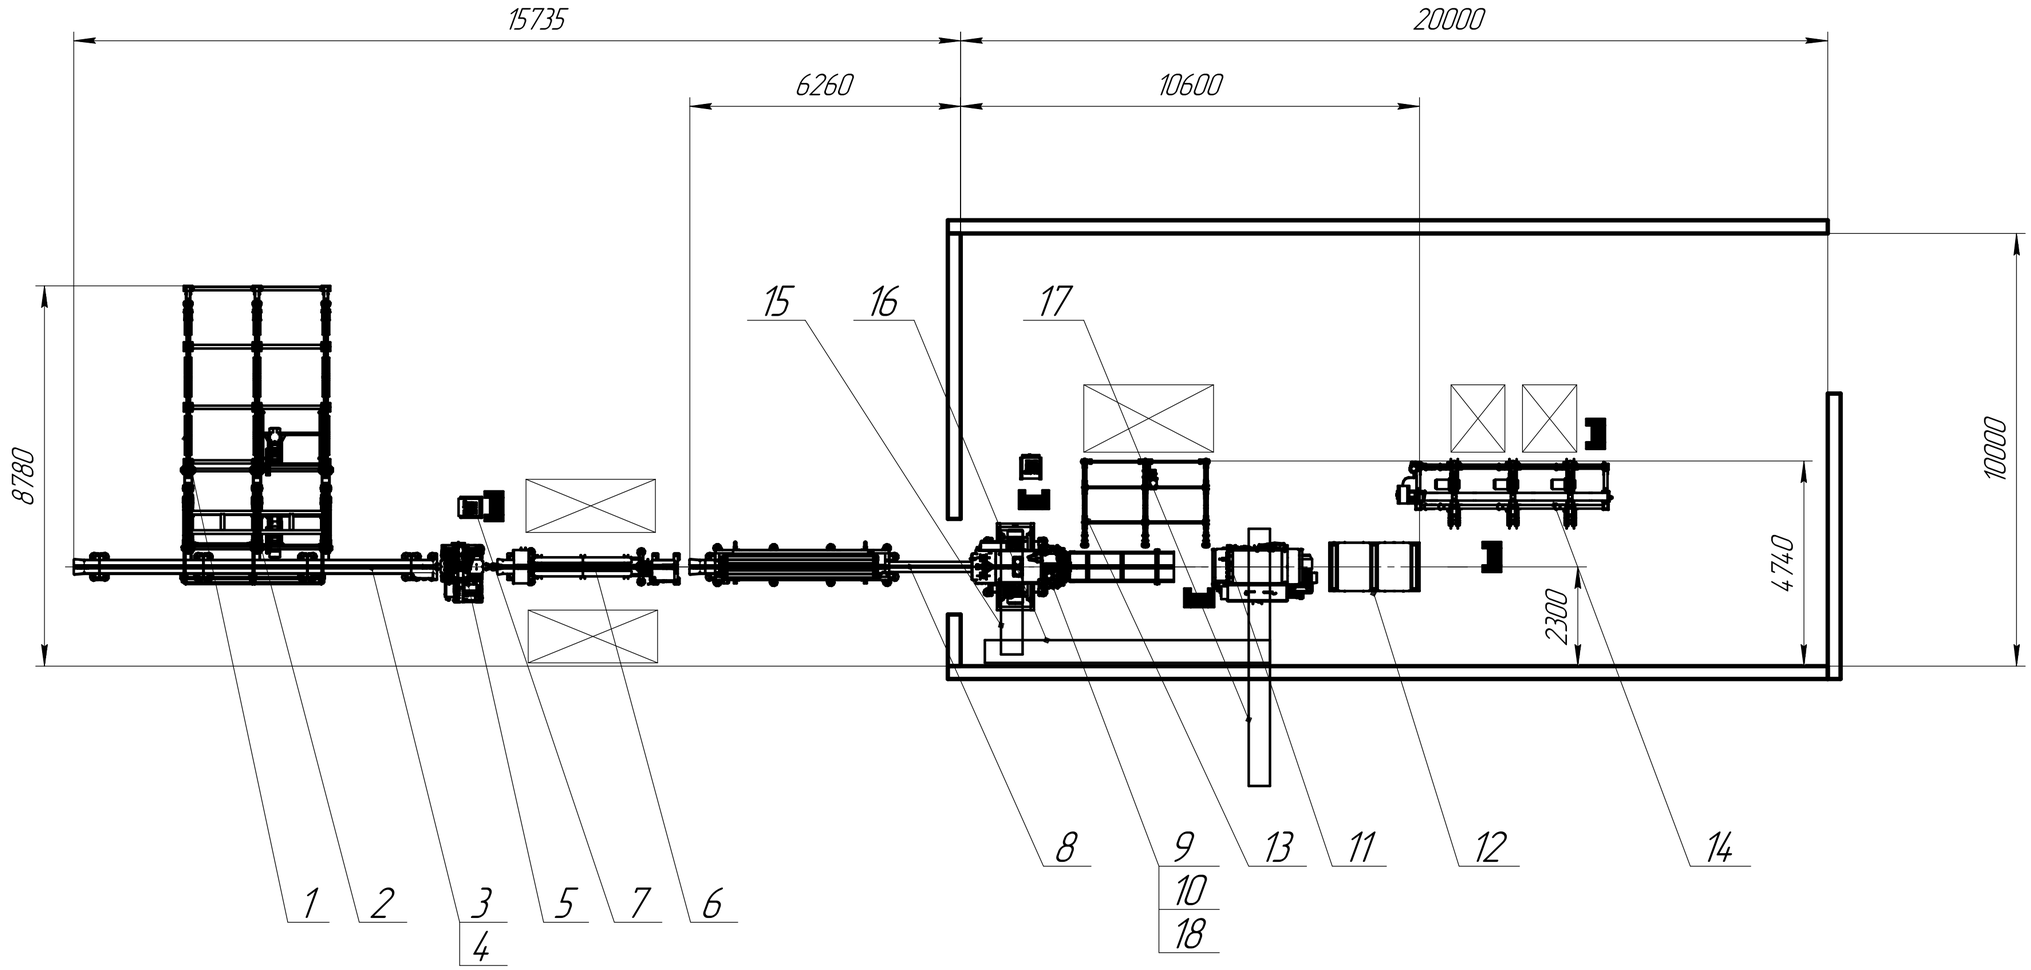

Поз.	Наименование	Кол-во	Примечание
1	Накопитель для бревен НБ25Т 6-4	1	
2	Перегружатель бревен ПБ-6-01	1	
3	Стол-комплект Б50 ЗУБ_ВЗ-7,8 СБ	1	
4	Бревнотаска с зубчиками БТЗ-500 3 кВт	1	
5	Станок торцовки бревен СТБ-450П_А	1	
6	Сбрасыватель бревен двусторонний СБД 3-500	1	
7	Комплексное управление оборудованием	1	Упр: 1-6
8	Стол-комплект С76 ЗУБ_Вр-7	1	
9	Станок для тонкомера Триумф С-750 М_22 без стола	1	
10	Стол С 2,4Х_25,4 С76 СБ	1	
11	Одновальный многопильный станок Триумф Б700 (55кВт)	1	
12	Рольганг закрытый Р-1000-2	1	
13	Транспортер цепной поперечный ТЦП 3х2	1	
14	Станок мультиторцовочный Триумф ТСМ3 100-3	1	
15	Конвейер скребковый КС 400 (3х1м)	1	
16	Конвейер скребковый КС 340 (2х2,5м+1х1м)	1	
17	Конвейер скребковый КСП 500 (3х2,5м)***	1	
18	Пульт управления ТР-3.36-01	1	

Поз. 12,13 может устанавливаться согласно технологии производства в месте свободного доступа Оператора.

Полный комплект технической документации предоставляется после согласования предварительной схемы.
Для установки транспортеров необходимы траншеи.

Параметры вход. материала:
Высота вход. окна = max 320 мм,
L = 6 ±0,2 м. После поз.5 L = 3 ±0,2
Потребление линии до 160 кВт.
Производительность до 10 куб.м./час..

Изм.	Лист	№ докум.	Подп.	Дата	0948-2 Проект		
Разраб.		Шишкин Е.				Лит. / Масса / Масштаб 1:100	
Пров.							
Т.контр.						Лист / Листов 1	
Н.контр.					Приложение 1	ООО "Завод"Энерготех"	
Утв.							

Перв. примен. | Справ. № | Подп. и дата | Инв. № дубл. | Взам. инв. № | Подп. и дата | Инв. № подл.

Копировал | Формат А2